



Cairn Youth Centre - room squares at 1:200

Program v0.7 net areas; each square's side = sqrt(area). Net 1,904 m² × 1.3 ≈ gross 2,476 m² (circulation + walls not shown). PRINT AT 100% / ACTUAL SIZE.

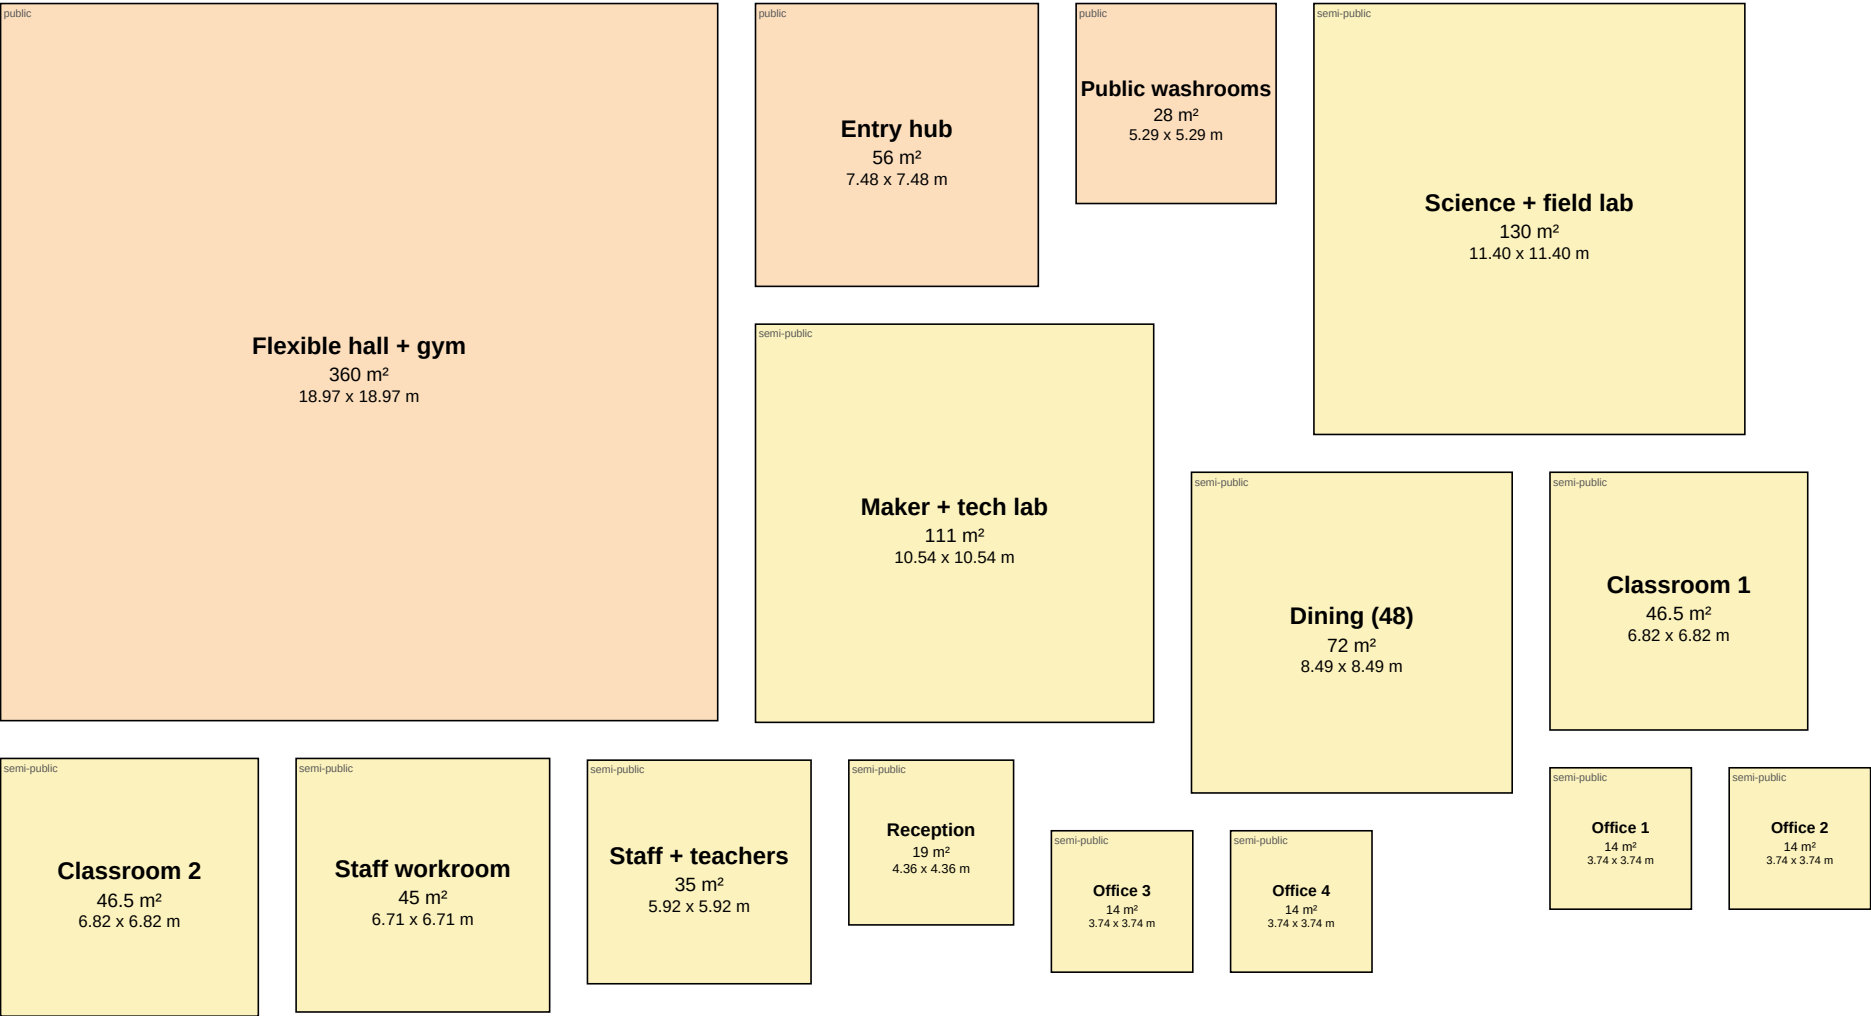




- Public
- Semi-Public
- Private
- Expedition
- Service
- Mechanical

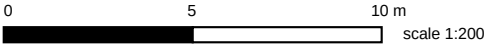

Print check: this bar must measure 100 mm

Cairn Youth Centre - room squares at 1:200

Program v0.7 net areas; each square's side = sqrt(area). Net 1,904 m² × 1.3 ≈ gross 2,476 m² (circulation + walls not shown). PRINT AT 100% / ACTUAL SIZE.

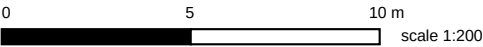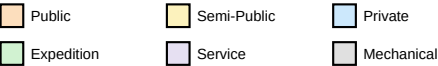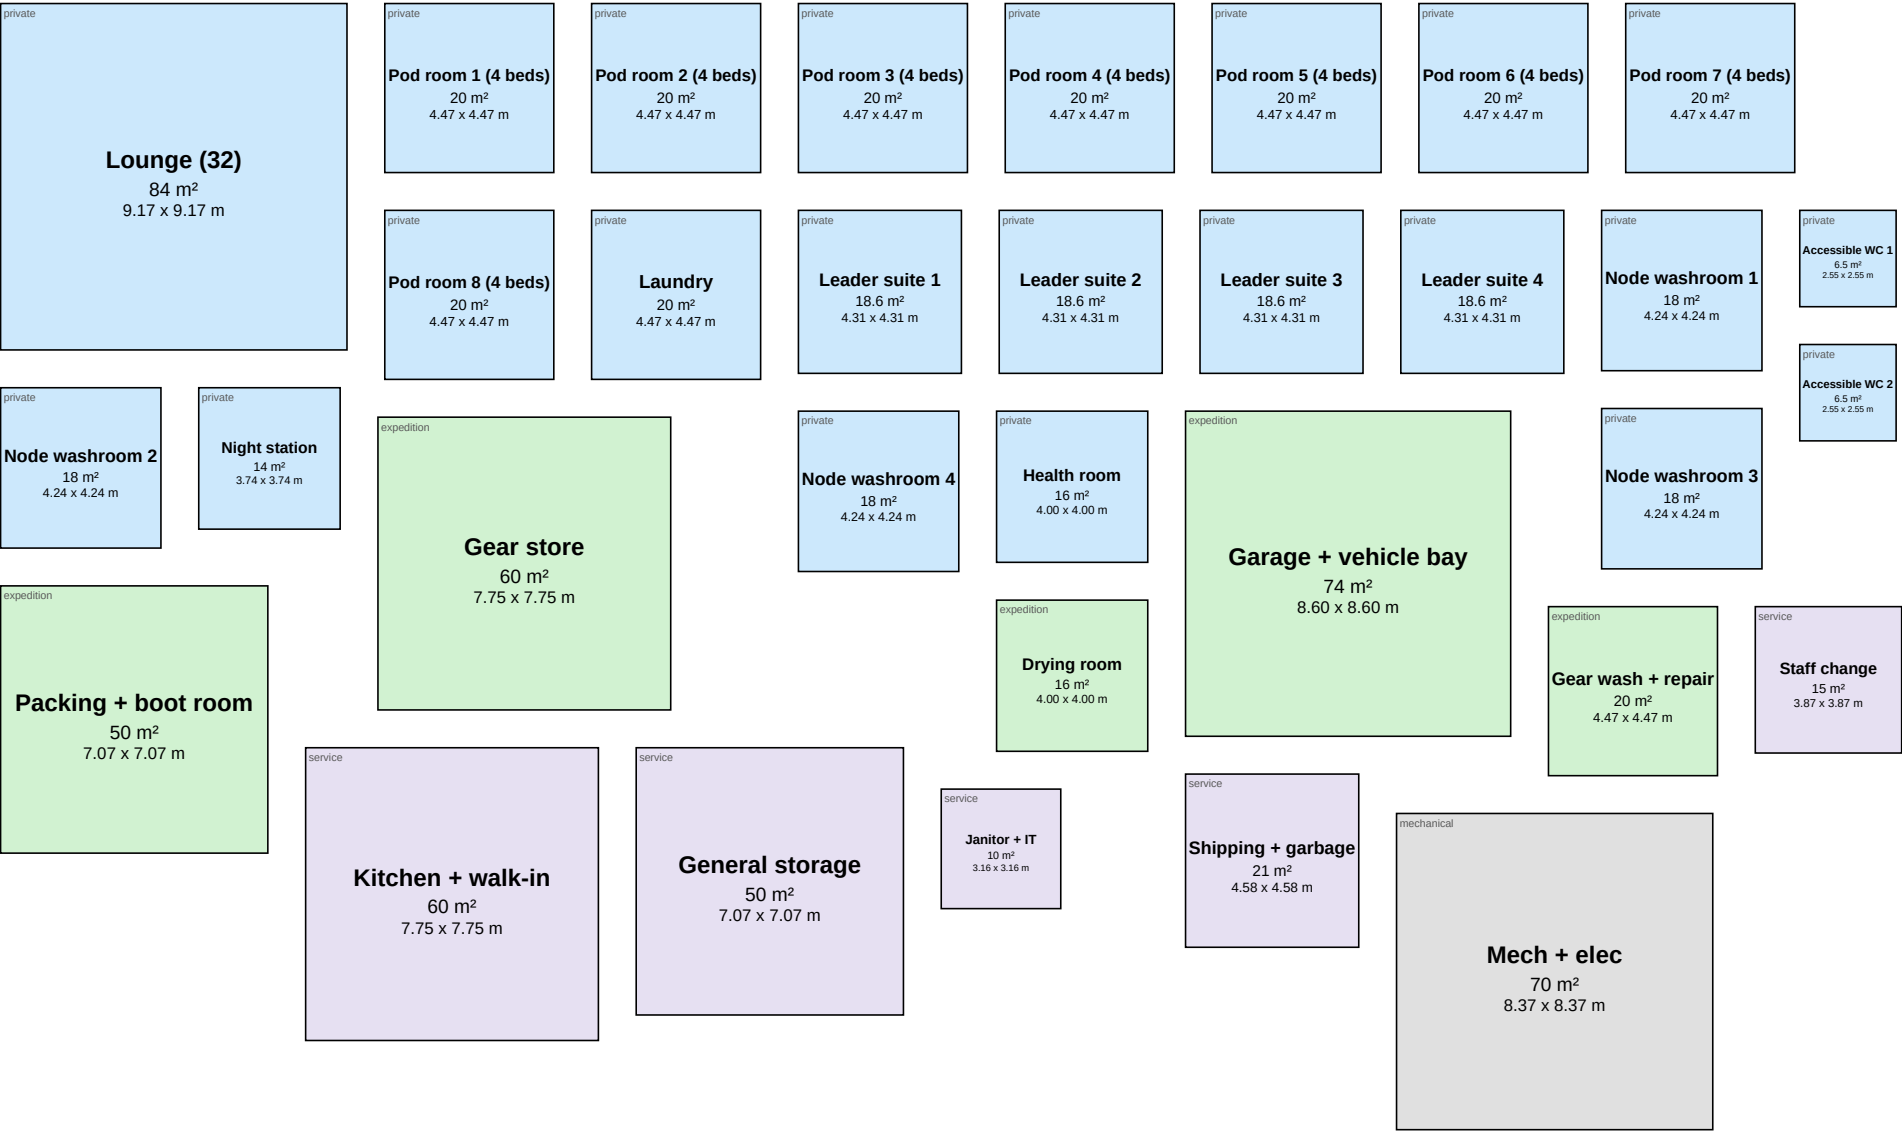

Print check: this bar must measure 100 mm



Cairn Youth Centre - room squares at 1:200

Program v0.7 net areas; each square's side = sqrt(area). Net 1,904 m² × 1.3 ≈ gross 2,476 m² (circulation + walls not shown). PRINT AT 100% / ACTUAL SIZE.



- Public

Semi-Public

Private

Expedition

Service

Mechanical

